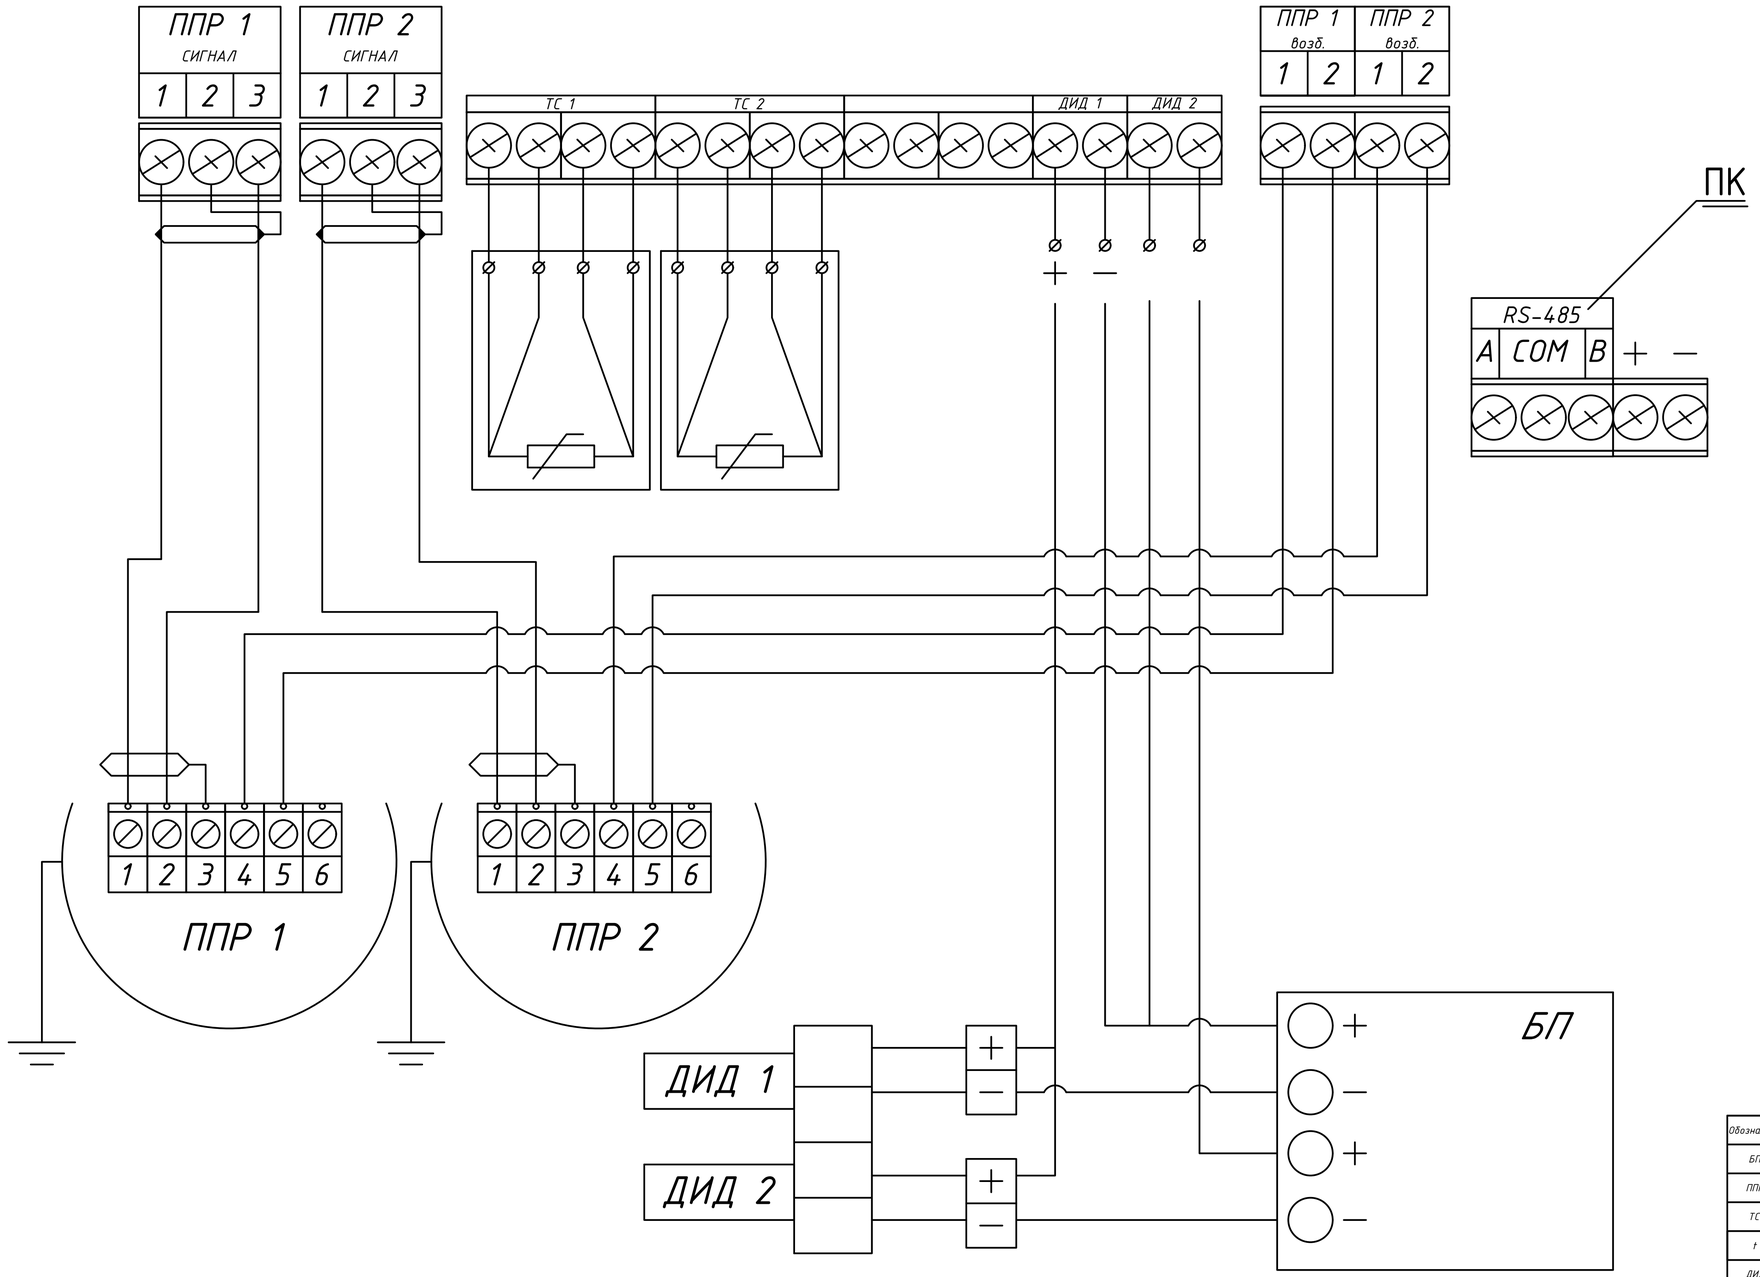

Обозначение	Наименование	Кол-во
БП	Блок питания	1
ППР	Первичный преобразователь расхода	2
ТС	Термопреобразователь сопротивления	2
t	Минимальное измеряемое значение разности температур между подающим и обратным трубопроводами	2
ДИД	Датчик избыточного давления	2
ПК	IBM-совместимый персональный компьютер	1

					С 15.02.07 21			
Изм.	Кол.	Фамилия	Подп.	Дата	Разработка системы автоматизации теплового пункта многоэтажного жилого здания	Лит.	Масса	Масштаб
Студент		Новоселов А.А.				У		
Консул.		Зайкова Т.Г.				Лист 2	Листов 2	
Н. контр.		Чекунова А.С.						
					Принципиальная схема	ПК-312-А		

220301 14. 00